
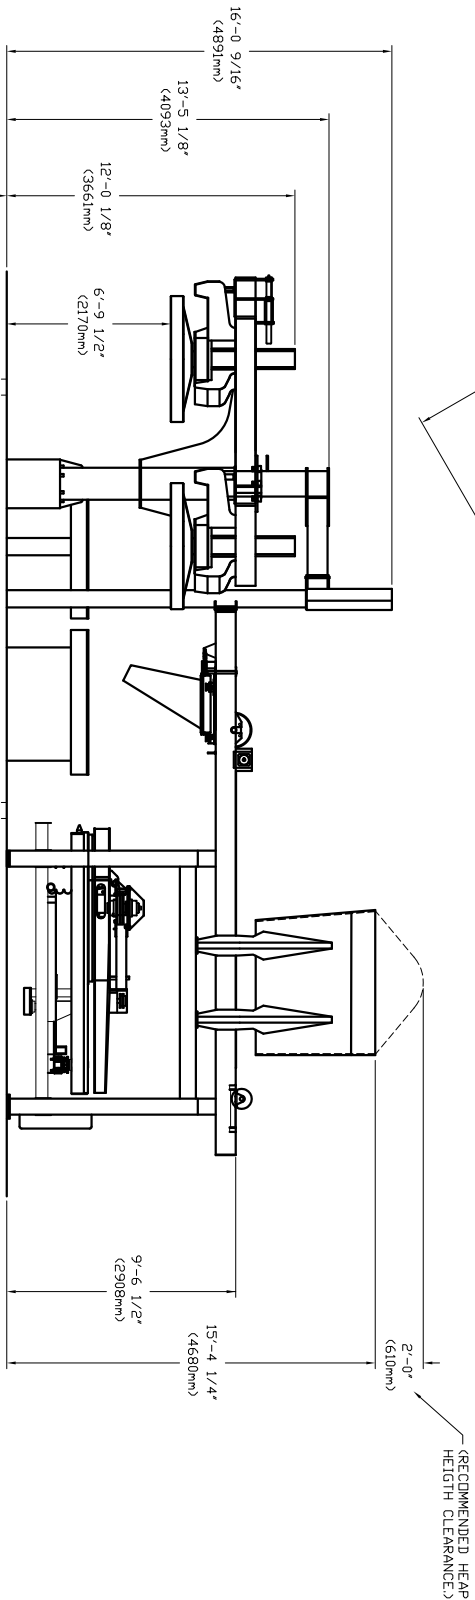


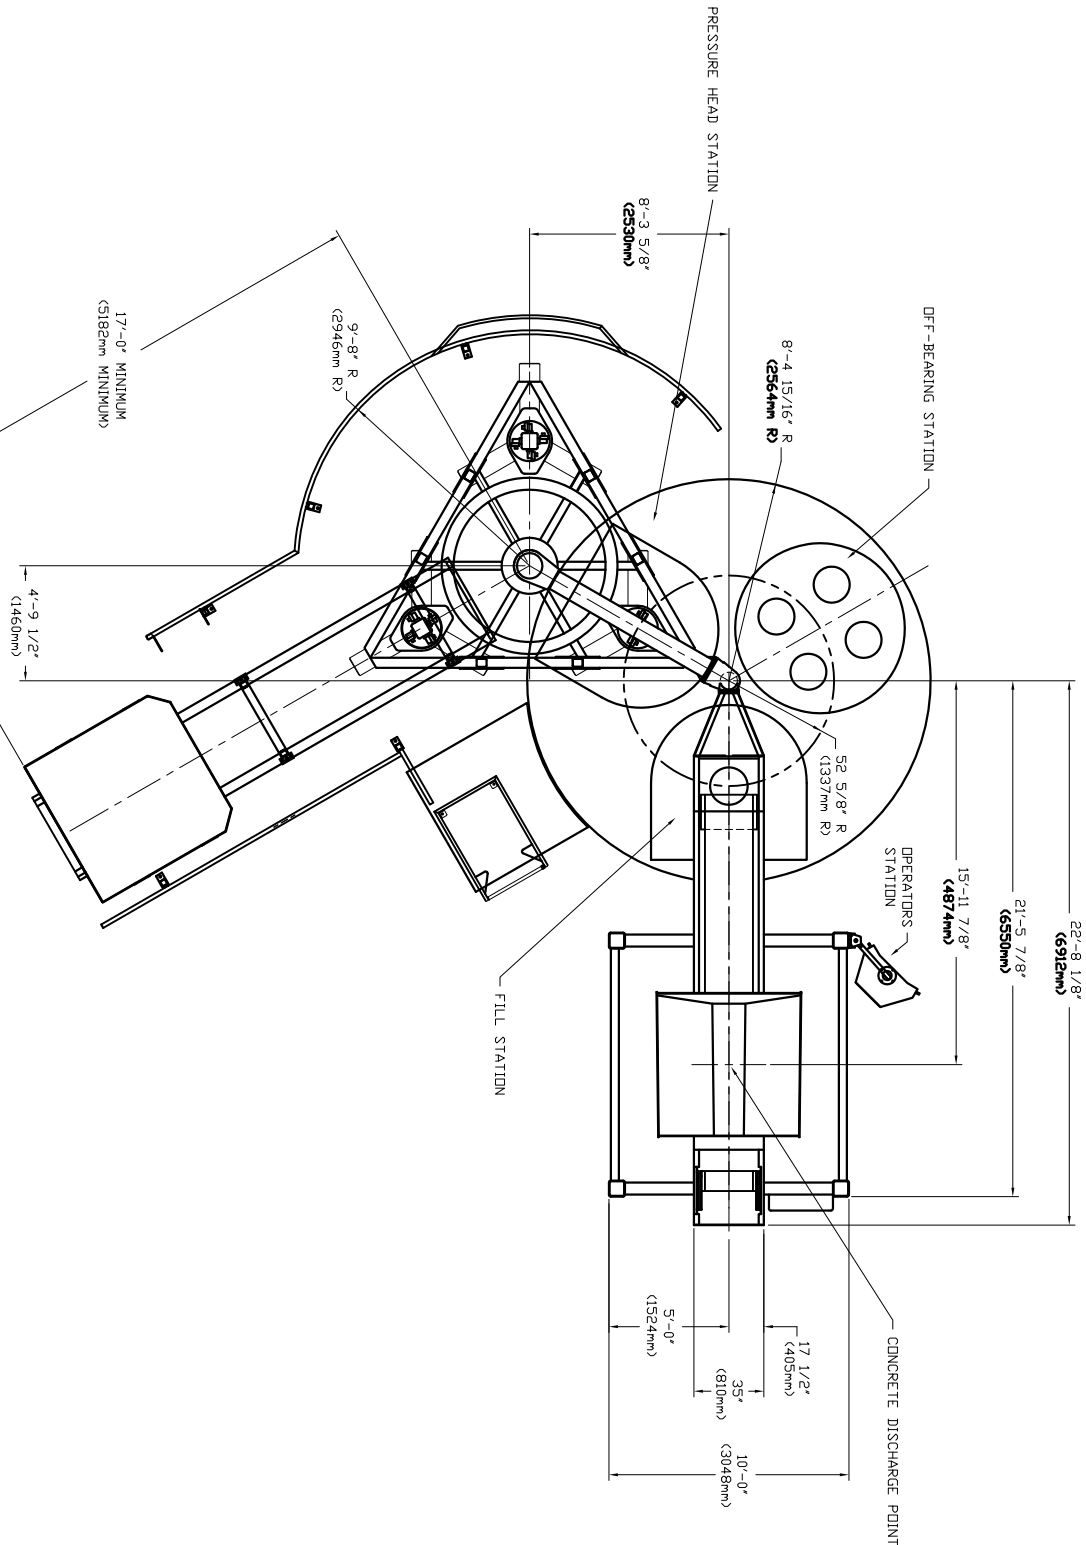

(SEE FOUNDATION DVG.)

HAWKEYE CONCRETE PRODUCTS CO.									
MEDIAPOLIS, INDIA									
PIPE PRO III STANDARD IMAGE MACHINE, 0° FEEDER									
WITH IN-LINE HEADER TRANSFER CART									
TOLERANCES (UNLESS SPECIFIED)									
SCALE	DATE	DRAWN	APPR	ANGULAR	FILE NO.	DIR	PP3	DRAWING NO.	ISSUE
1=48	19940603	BSA			18-2			29551D	A