


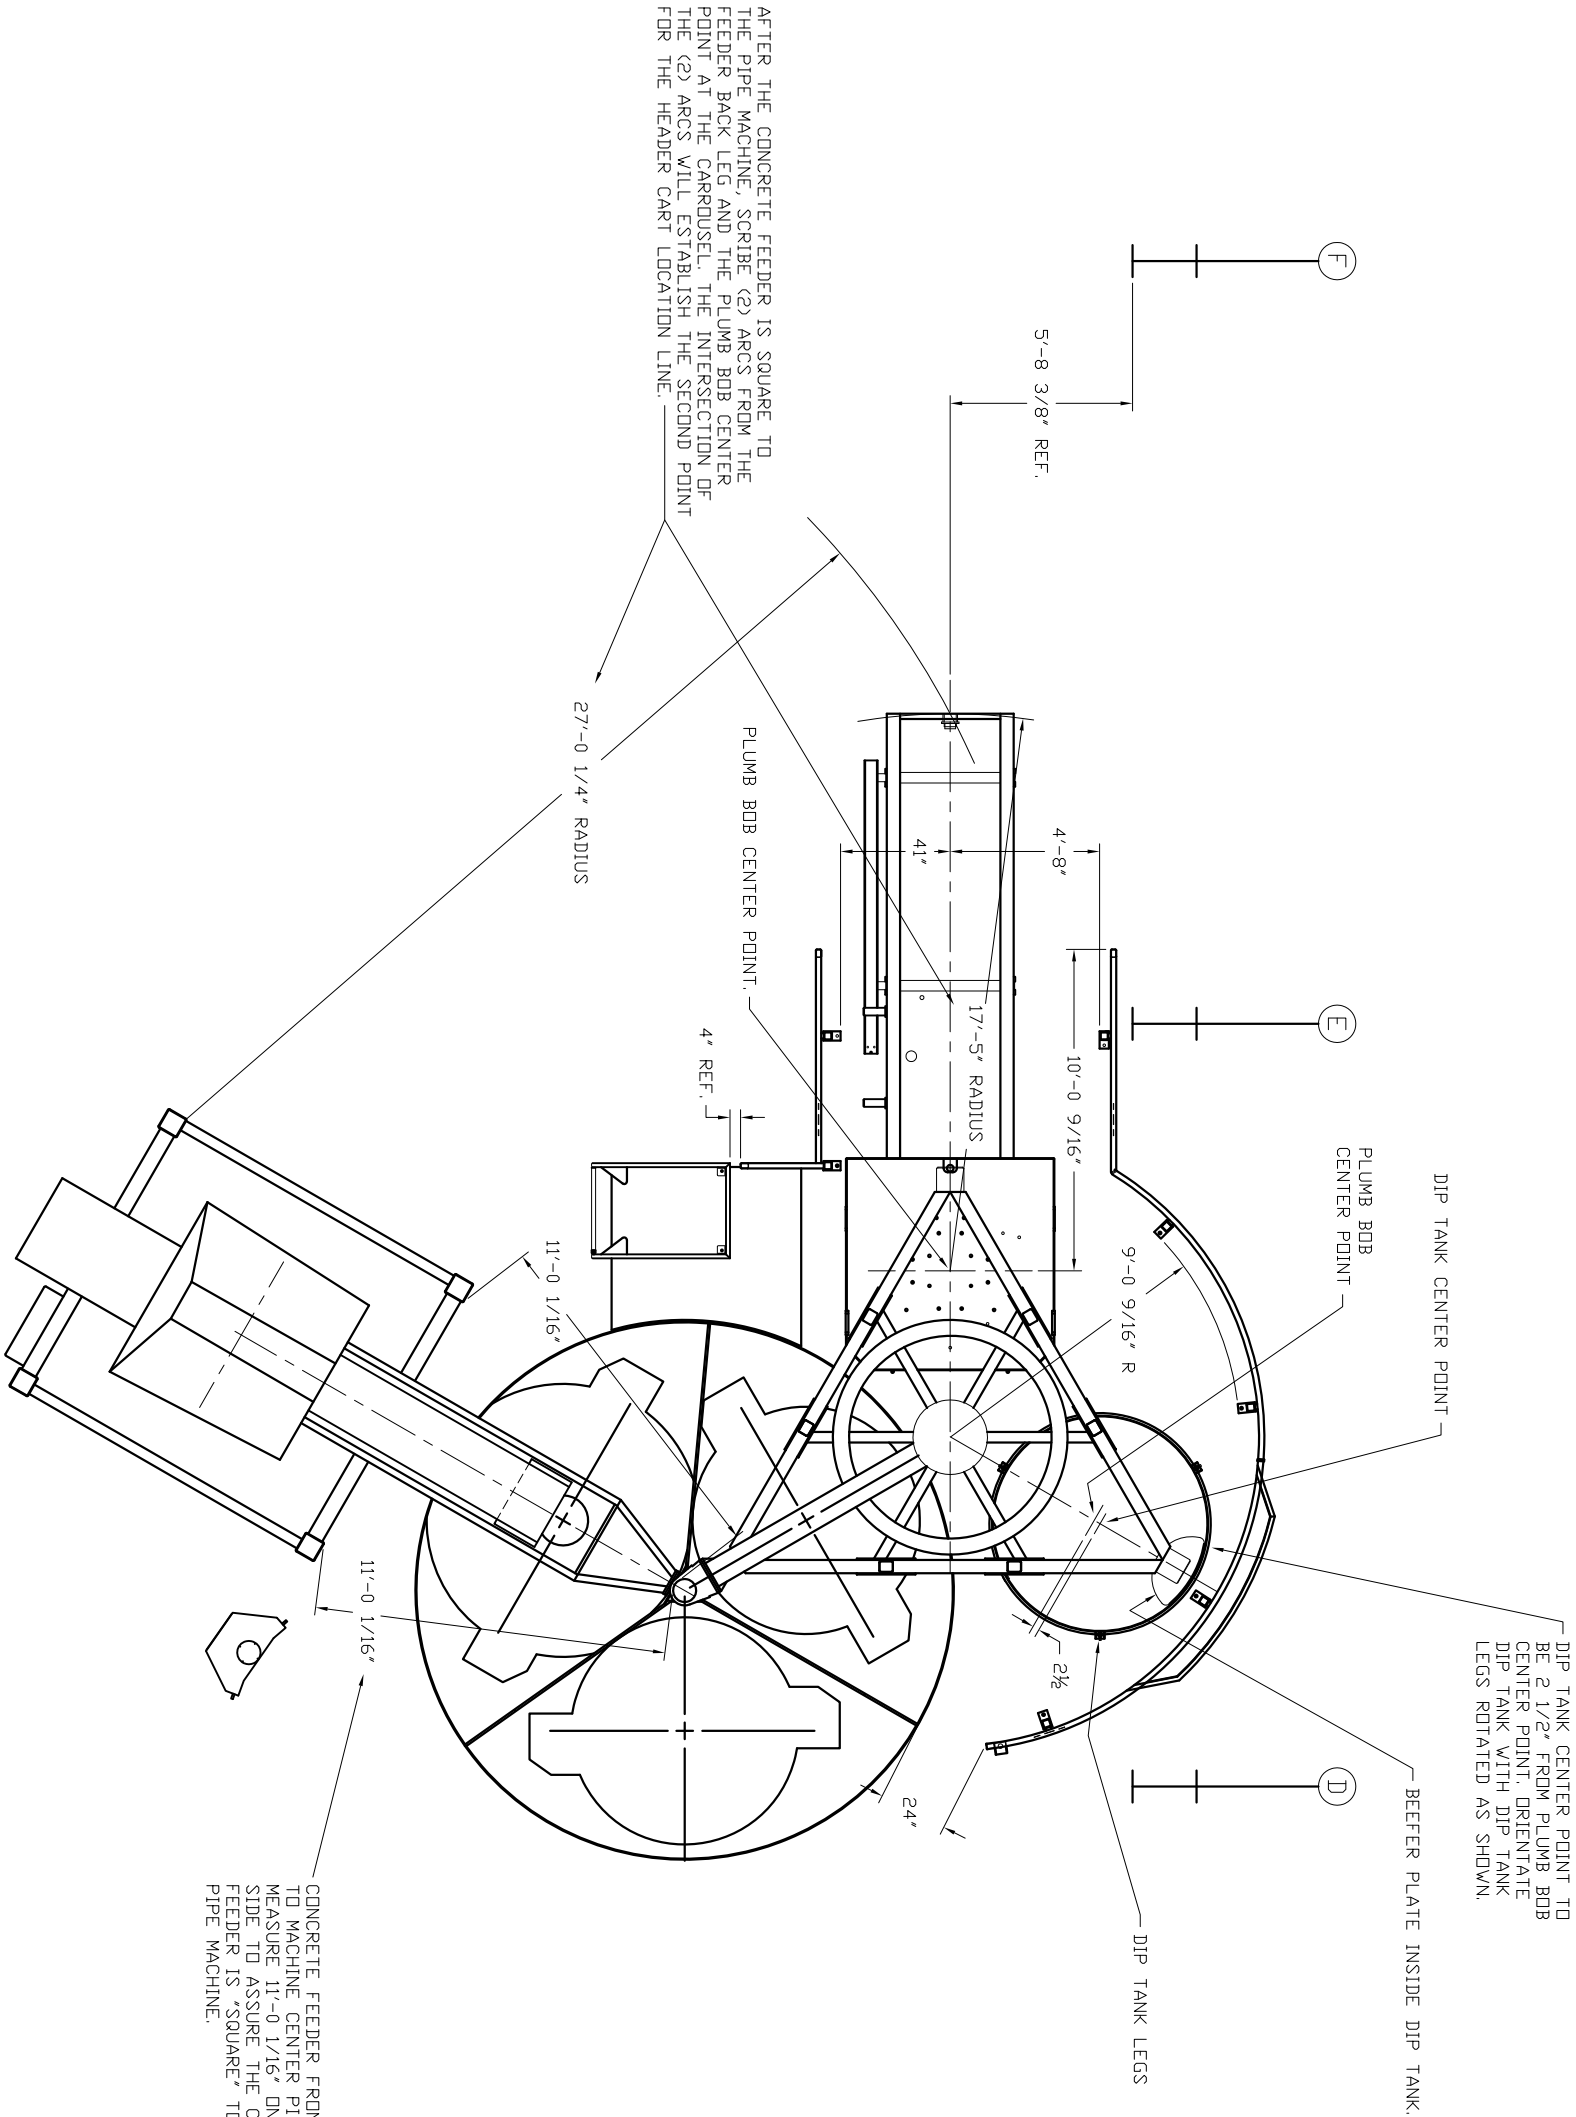

HAWKEYE CONCRETE PRODUCTS CO.									
MEDIAPOLIS, INDIA									
PIPE PRD III MACHINE COMPONENT PLACEMENT									
FOR PEACE DALE PRECAST									
TOLERANCES (UNLESS SPECIFIED)					DIR				
FRACTIONAL ±1/16	DECIMAL	ANGULAR	FILE NO.	PP3	DRAWING NO.				
SCALE	DATE	DRAWN	APPR	26-1	29955C				
1/4"=1'	19940927	BSA			A				